


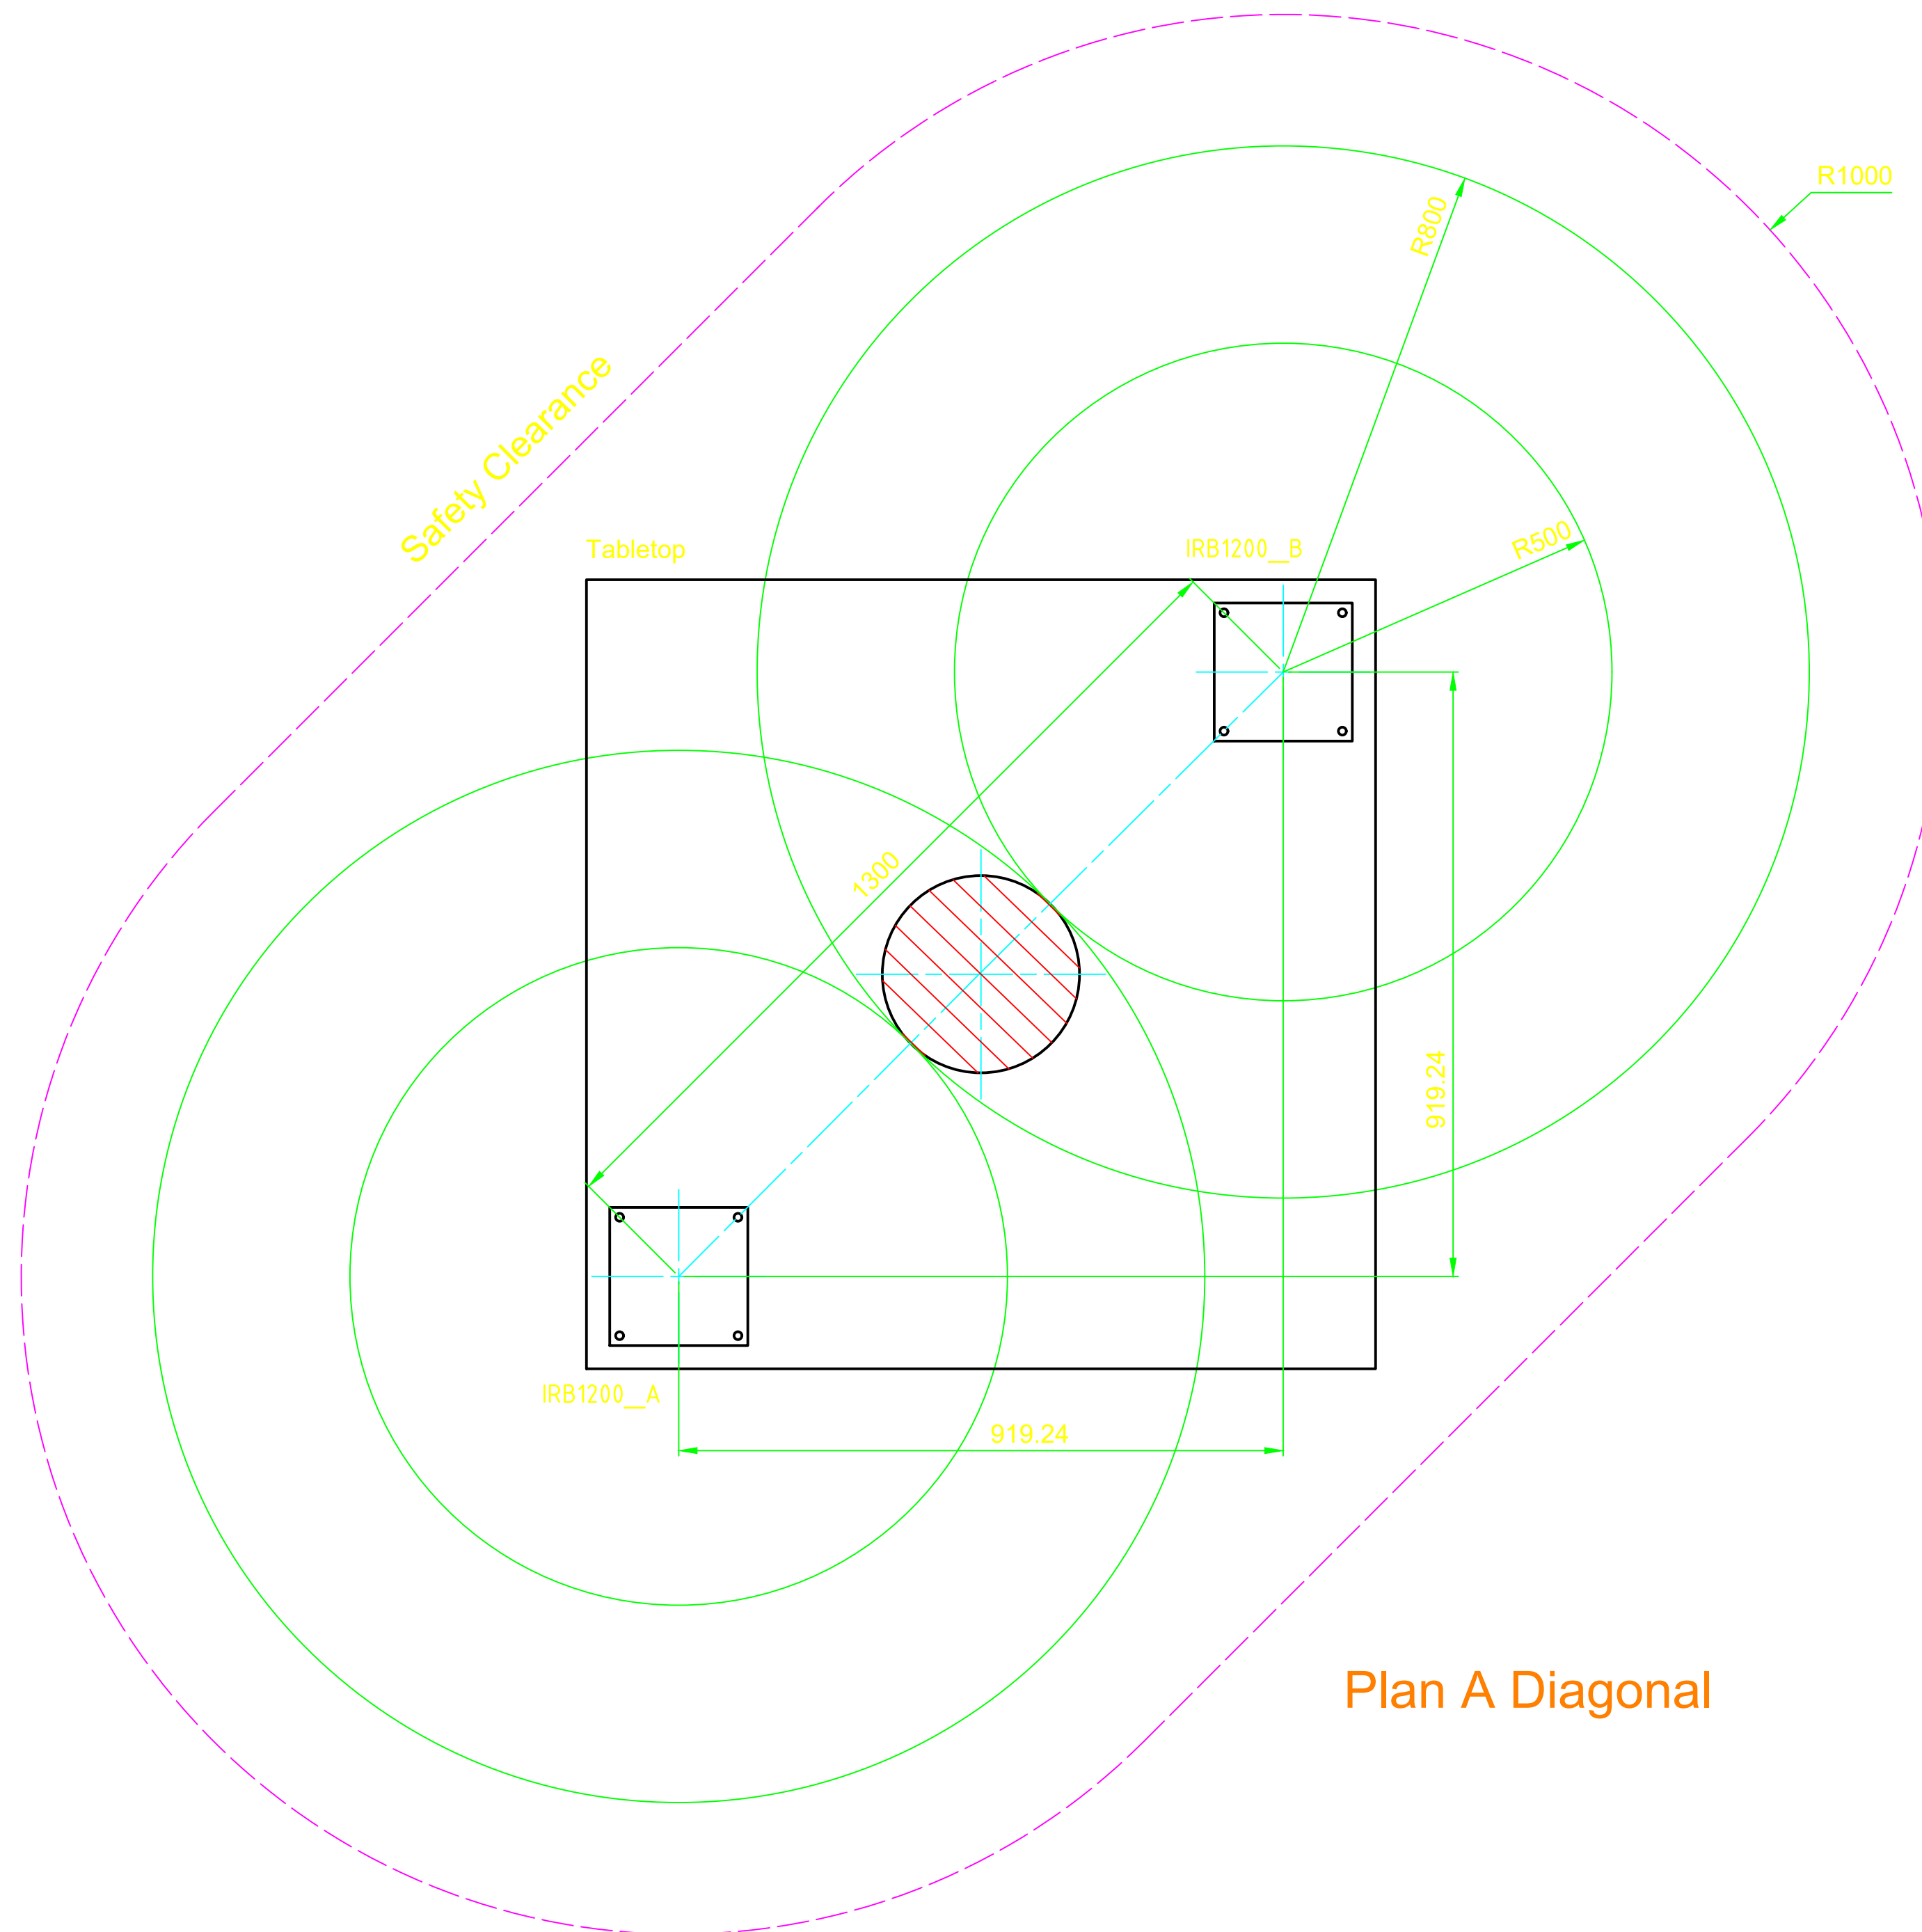

Plan A Diagonal